



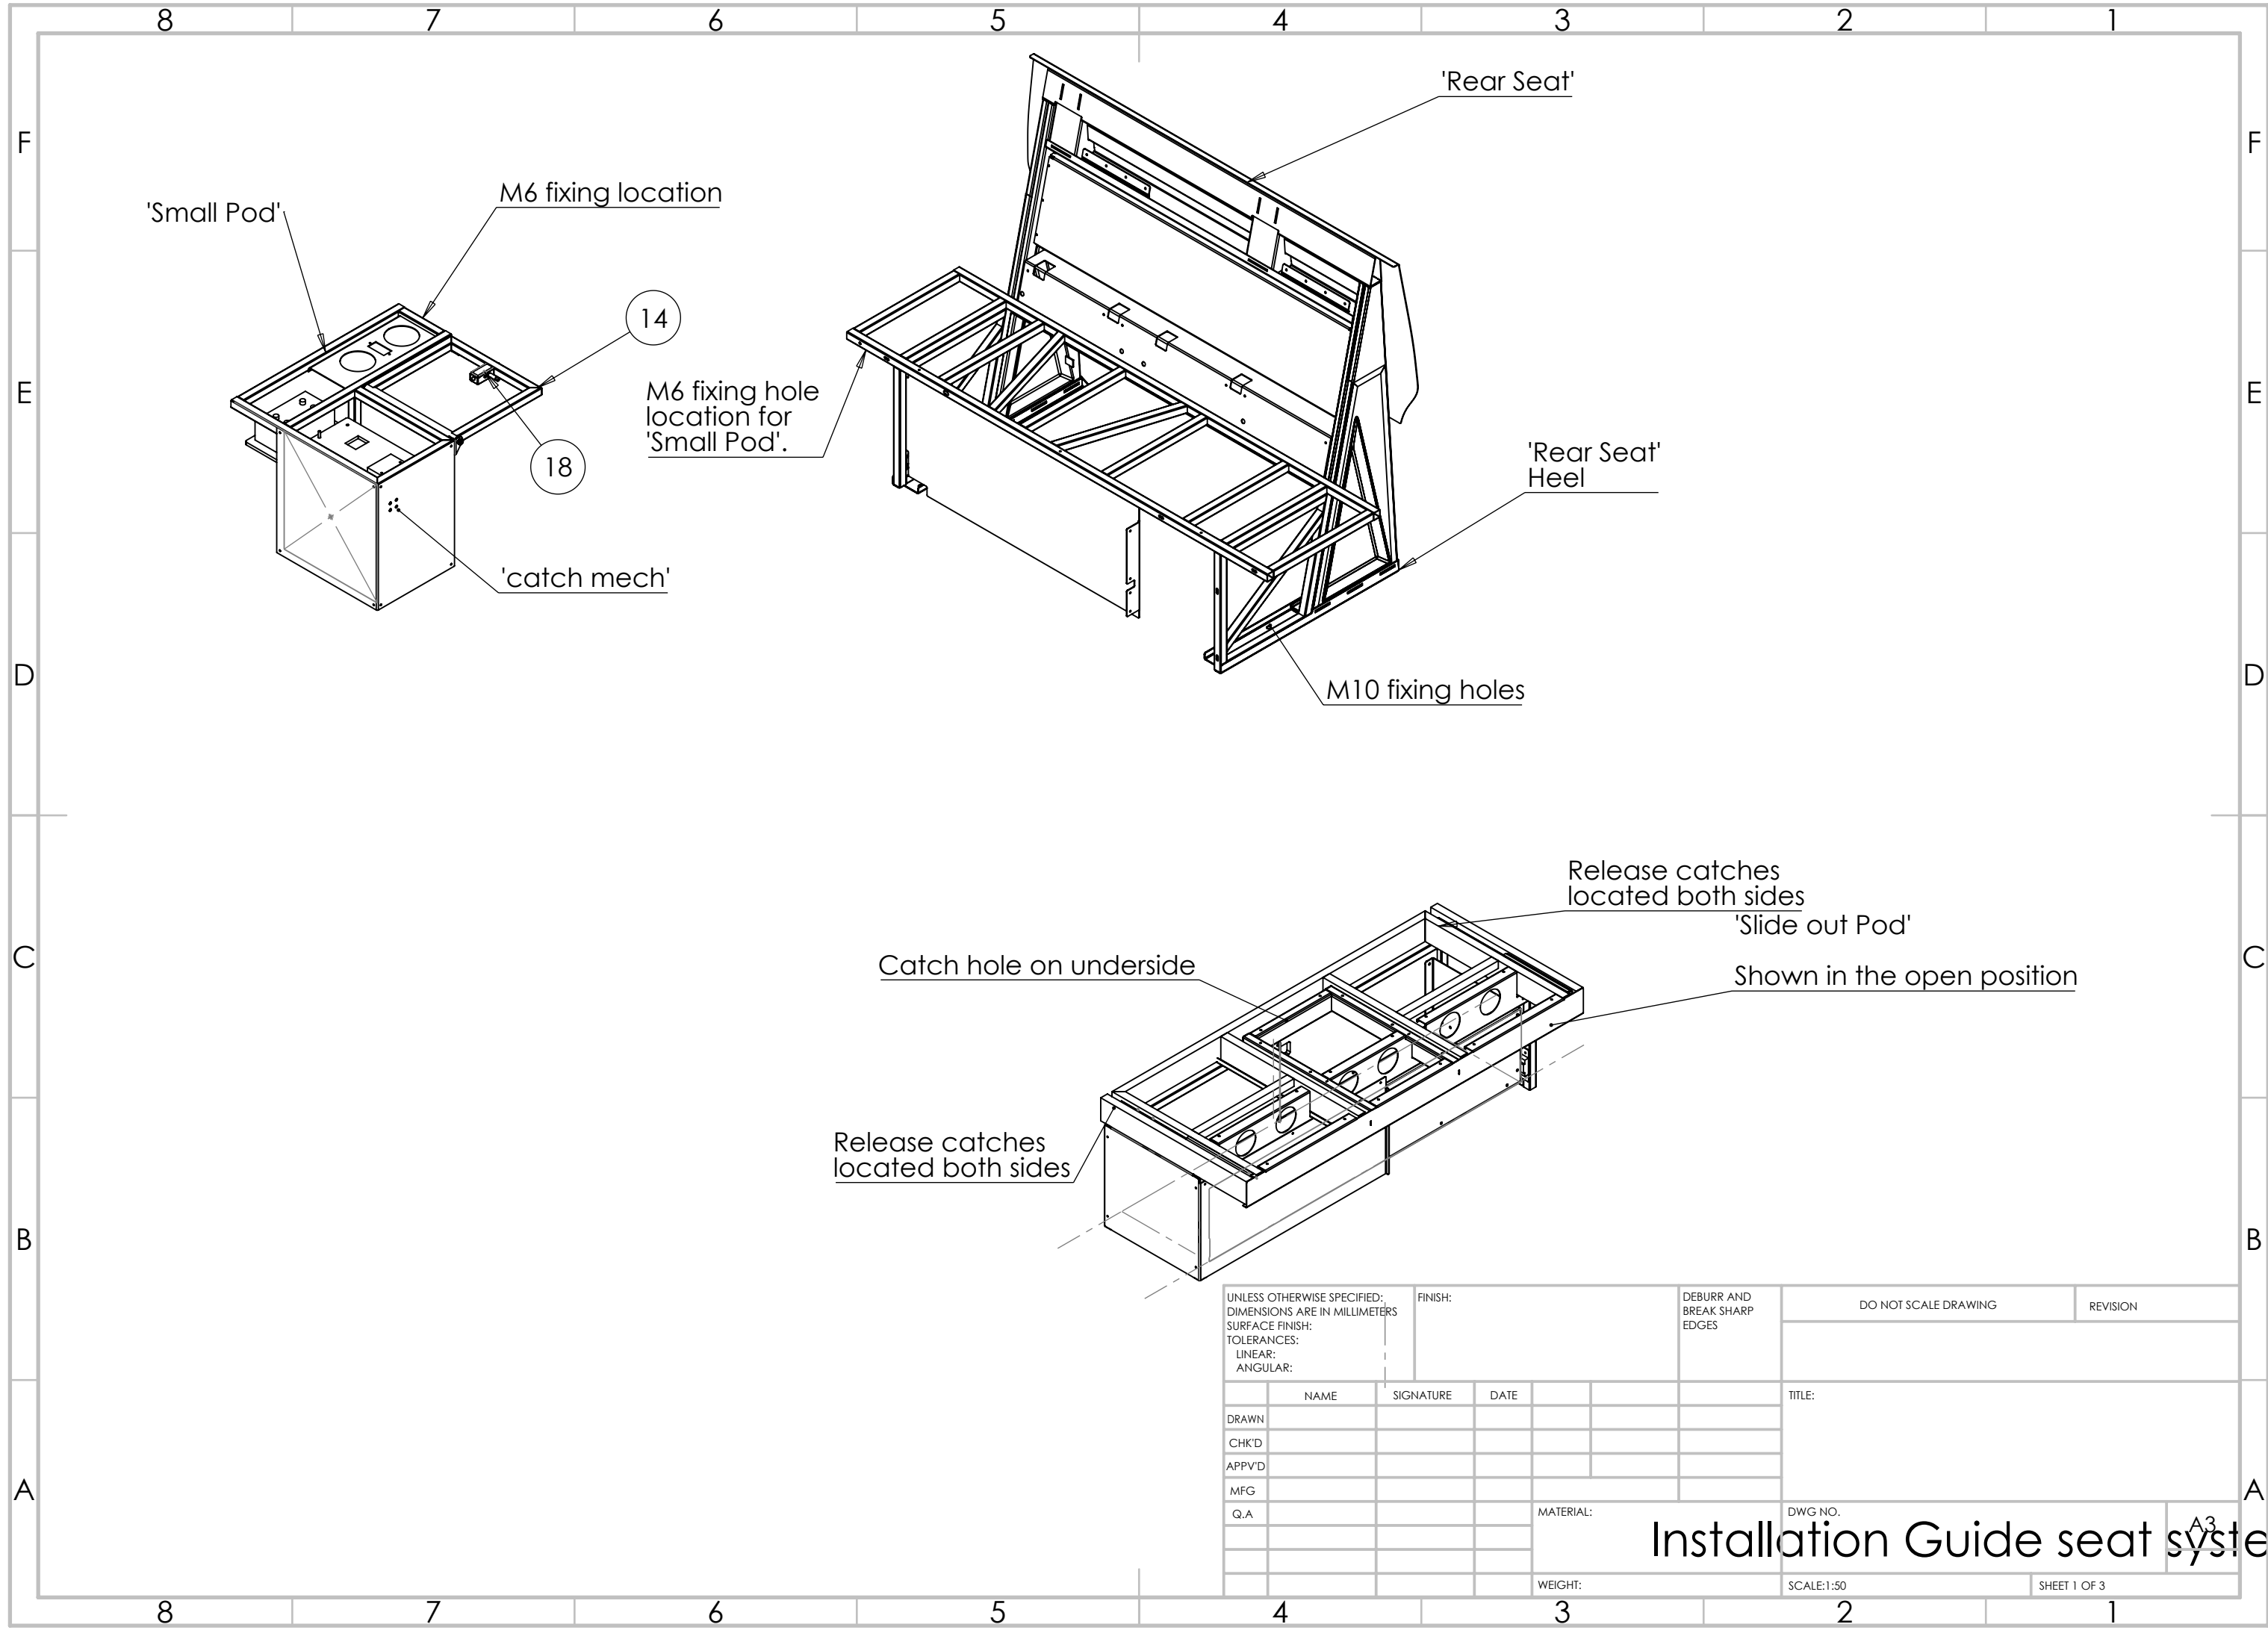

|   |  |  |  |         |  |                                    |  |                      |  |          |  |
|---|--|--|--|---------|--|------------------------------------|--|----------------------|--|----------|--|
| UNLESS OTHERWISE SPECIFIED;<br>DIMENSIONS ARE IN MILLIMETERS<br>SURFACE FINISH:<br>TOLERANCES:<br>LINEAR:<br>ANGULAR: |  |  |  | FINISH: |  | DEBURR AND<br>BREAK SHARP<br>EDGES |  | DO NOT SCALE DRAWING |  | REVISION |  |
|   |  |  |  |         |  |                                    |  |                      |  |          |  |
|   |  |  |  |         |  |                                    |  |                      |  |          |  |
|   |  |  |  |         |  |                                    |  |                      |  |          |  |
|   |  |  |  |         |  |                                    |  |                      |  |          |  |
|   |  |  |  |         |  |                                    |  |                      |  |          |  |
|   |  |  |  |         |  |                                    |  |                      |  |          |  |
|   |  |  |  |         |  |                                    |  |                      |  |          |  |
|   |  |  |  |         |  |                                    |  |                      |  |          |  |
|   |  |  |  |         |  |                                    |  |                      |  |          |  |
|   |  |  |  |         |  |                                    |  |                      |  |          |  |
|   |  |  |  |         |  |                                    |  |                      |  |          |  |
|   |  |  |  |         |  |                                    |  |                      |  |          |  |
|   |  |  |  |         |  |                                    |  |                      |  |          |  |
|   |  |  |  |         |  |                                    |  |                      |  |          |  |
|   |  |  |  |         |  |                                    |  |                      |  |          |  |
|   |  |  |  |         |  |                                    |  |                      |  |          |  |
|   |  |  |  |         |  |                                    |  |                      |  |          |  |
|   |  |  |  |         |  |                                    |  |                      |  |          |  |
|   |  |  |  |         |  |                                    |  |                      |  |          |  |
|   |  |  |  |         |  |                                    |  |                      |  |          |  |
|   |  |  |  |         |  |                                    |  |                      |  |          |  |
|   |  |  |  |         |  |                                    |  |                      |  |          |  |
|   |  |  |  |         |  |                                    |  |                      |  |          |  |
|   |  |  |  |         |  |                                    |  |                      |  |          |  |
|   |  |  |  |         |  |                                    |  |                      |  |          |  |
|   |  |  |  |         |  |                                    |  |                      |  |          |  |
|   |  |  |  |         |  |                                    |  |                      |  |          |  |
|   |  |  |  |         |  |                                    |  |                      |  |          |  |
|   |  |  |  |         |  |                                    |  |                      |  |          |  |
|   |  |  |  |         |  |                                    |  |                      |  |          |  |
|   |  |  |  |         |  |                                    |  |                      |  |          |  |
|   |  |  |  |         |  |                                    |  |                      |  |          |  |
|   |  |  |  |         |  |                                    |  |                      |  |          |  |
|   |  |  |  |         |  |                                    |  |                      |  |          |  |
|   |  |  |  |         |  |                                    |  |                      |  |          |  |
|   |  |  |  |         |  |                                    |  |                      |  |          |  |
|   |  |  |  |         |  |                                    |  |                      |  |          |  |
|   |  |  |  |         |  |                                    |  |                      |  |          |  |
|   |  |  |  |         |  |                                    |  |                      |  |          |  |
|   |  |  |  |         |  |                                    |  |                      |  |          |  |
|   |  |  |  |         |  |                                    |  |                      |  |          |  |
|   |  |  |  |         |  |                                    |  |                      |  |          |  |
|   |  |  |  |         |  |                                    |  |                      |  |          |  |
|   |  |  |  |         |  |                                    |  |                      |  |          |  |
|   |  |  |  |         |  |                                    |  |                      |  |          |  |
|   |  |  |  |         |  |                                    |  |                      |  |          |  |
|   |  |  |  |         |  |                                    |  |                      |  |          |  |
|   |  |  |  |         |  |                                    |  |                      |  |          |  |
|   |  |  |  |         |  |                                    |  |                      |  |          |  |
|   |  |  |  |         |  |                                    |  |                      |  |          |  |
|   |  |  |  |         |  |                                    |  |                      |  |          |  |
|   |  |  |  |         |  |                                    |  |                      |  |          |  |
|   |  |  |  |         |  |                                    |  |                      |  |          |  |
|   |  |  |  |         |  |                                    |  |                      |  |          |  |
|   |  |  |  |         |  |                                    |  |                      |  |          |  |
|   |  |  |  |         |  |                                    |  |                      |  |          |  |
|   |  |  |  |         |  |                                    |  |                      |  |          |  |
|   |  |  |  |         |  |                                    |  |                      |  |          |  |
|   |  |  |  |         |  |                                    |  |                      |  |          |  |
|   |  |  |  |         |  |                                    |  |                      |  |          |  |
|   |  |  |  |         |  |                                    |  |                      |  |          |  |
|   |  |  |  |         |  |                                    |  |                      |  |          |  |
|   |  |  |  |         |  |                                    |  |                      |  |          |  |
|   |  |  |  |         |  |                                    |  |                      |  |          |  |
|   |  |  |  |         |  |                                    |  |                      |  |          |  |
|   |  |  |  |         |  |                                    |  |                      |  |          |  |
|   |  |  |  |         |  |                                    |  |                      |  |          |  |
|   |  |  |  |         |  |                                    |  |                      |  |          |  |
|   |  |  |  |         |  |                                    |  |                      |  |          |  |
|   |  |  |  |         |  |                                    |  |                      |  |          |  |
|   |  |  |  |         |  |                                    |  |                      |  |          |  |
|   |  |  |  |         |  |                                    |  |                      |  |          |  |
|   |  |  |  |         |  |                                    |  |                      |  |          |  |
|   |  |  |  |         |  |                                    |  |                      |  |          |  |
|   |  |  |  |         |  |                                    |  |                      |  |          |  |
|   |  |  |  |         |  |                                    |  |                      |  |          |  |
|   |  |  |  |         |  |                                    |  |                      |  |          |  |
|   |  |  |  |         |  |                                    |  |                      |  |          |  |
|   |  |  |  |         |  |                                    |  |                      |  |          |  |
|   |  |  |  |         |  |                                    |  |                      |  |          |  |
|   |  |  |  |         |  |                                    |  |                      |  |          |  |
|   |  |  |  |         |  |                                    |  |                      |  |          |  |
|   |  |  |  |         |  |                                    |  |                      |  |          |  |
|   |  |  |  |         |  |                                    |  |                      |  |          |  |
|   |  |  |  |         |  |                                    |  |                      |  |          |  |
|   |  |  |  |         |  |                                    |  |                      |  |          |  |
|   |  |  |  |         |  |                                    |  |                      |  |          |  |
|   |  |  |  |         |  |                                    |  |                      |  |          |  |
|   |  |  |  |         |  |                                    |  |                      |  |          |  |
|   |  |  |  |         |  |                                    |  |                      |  |          |  |
|   |  |  |  |         |  |                                    |  |                      |  |          |  |
|   |  |  |  |         |  |                                    |  |                      |  |          |  |



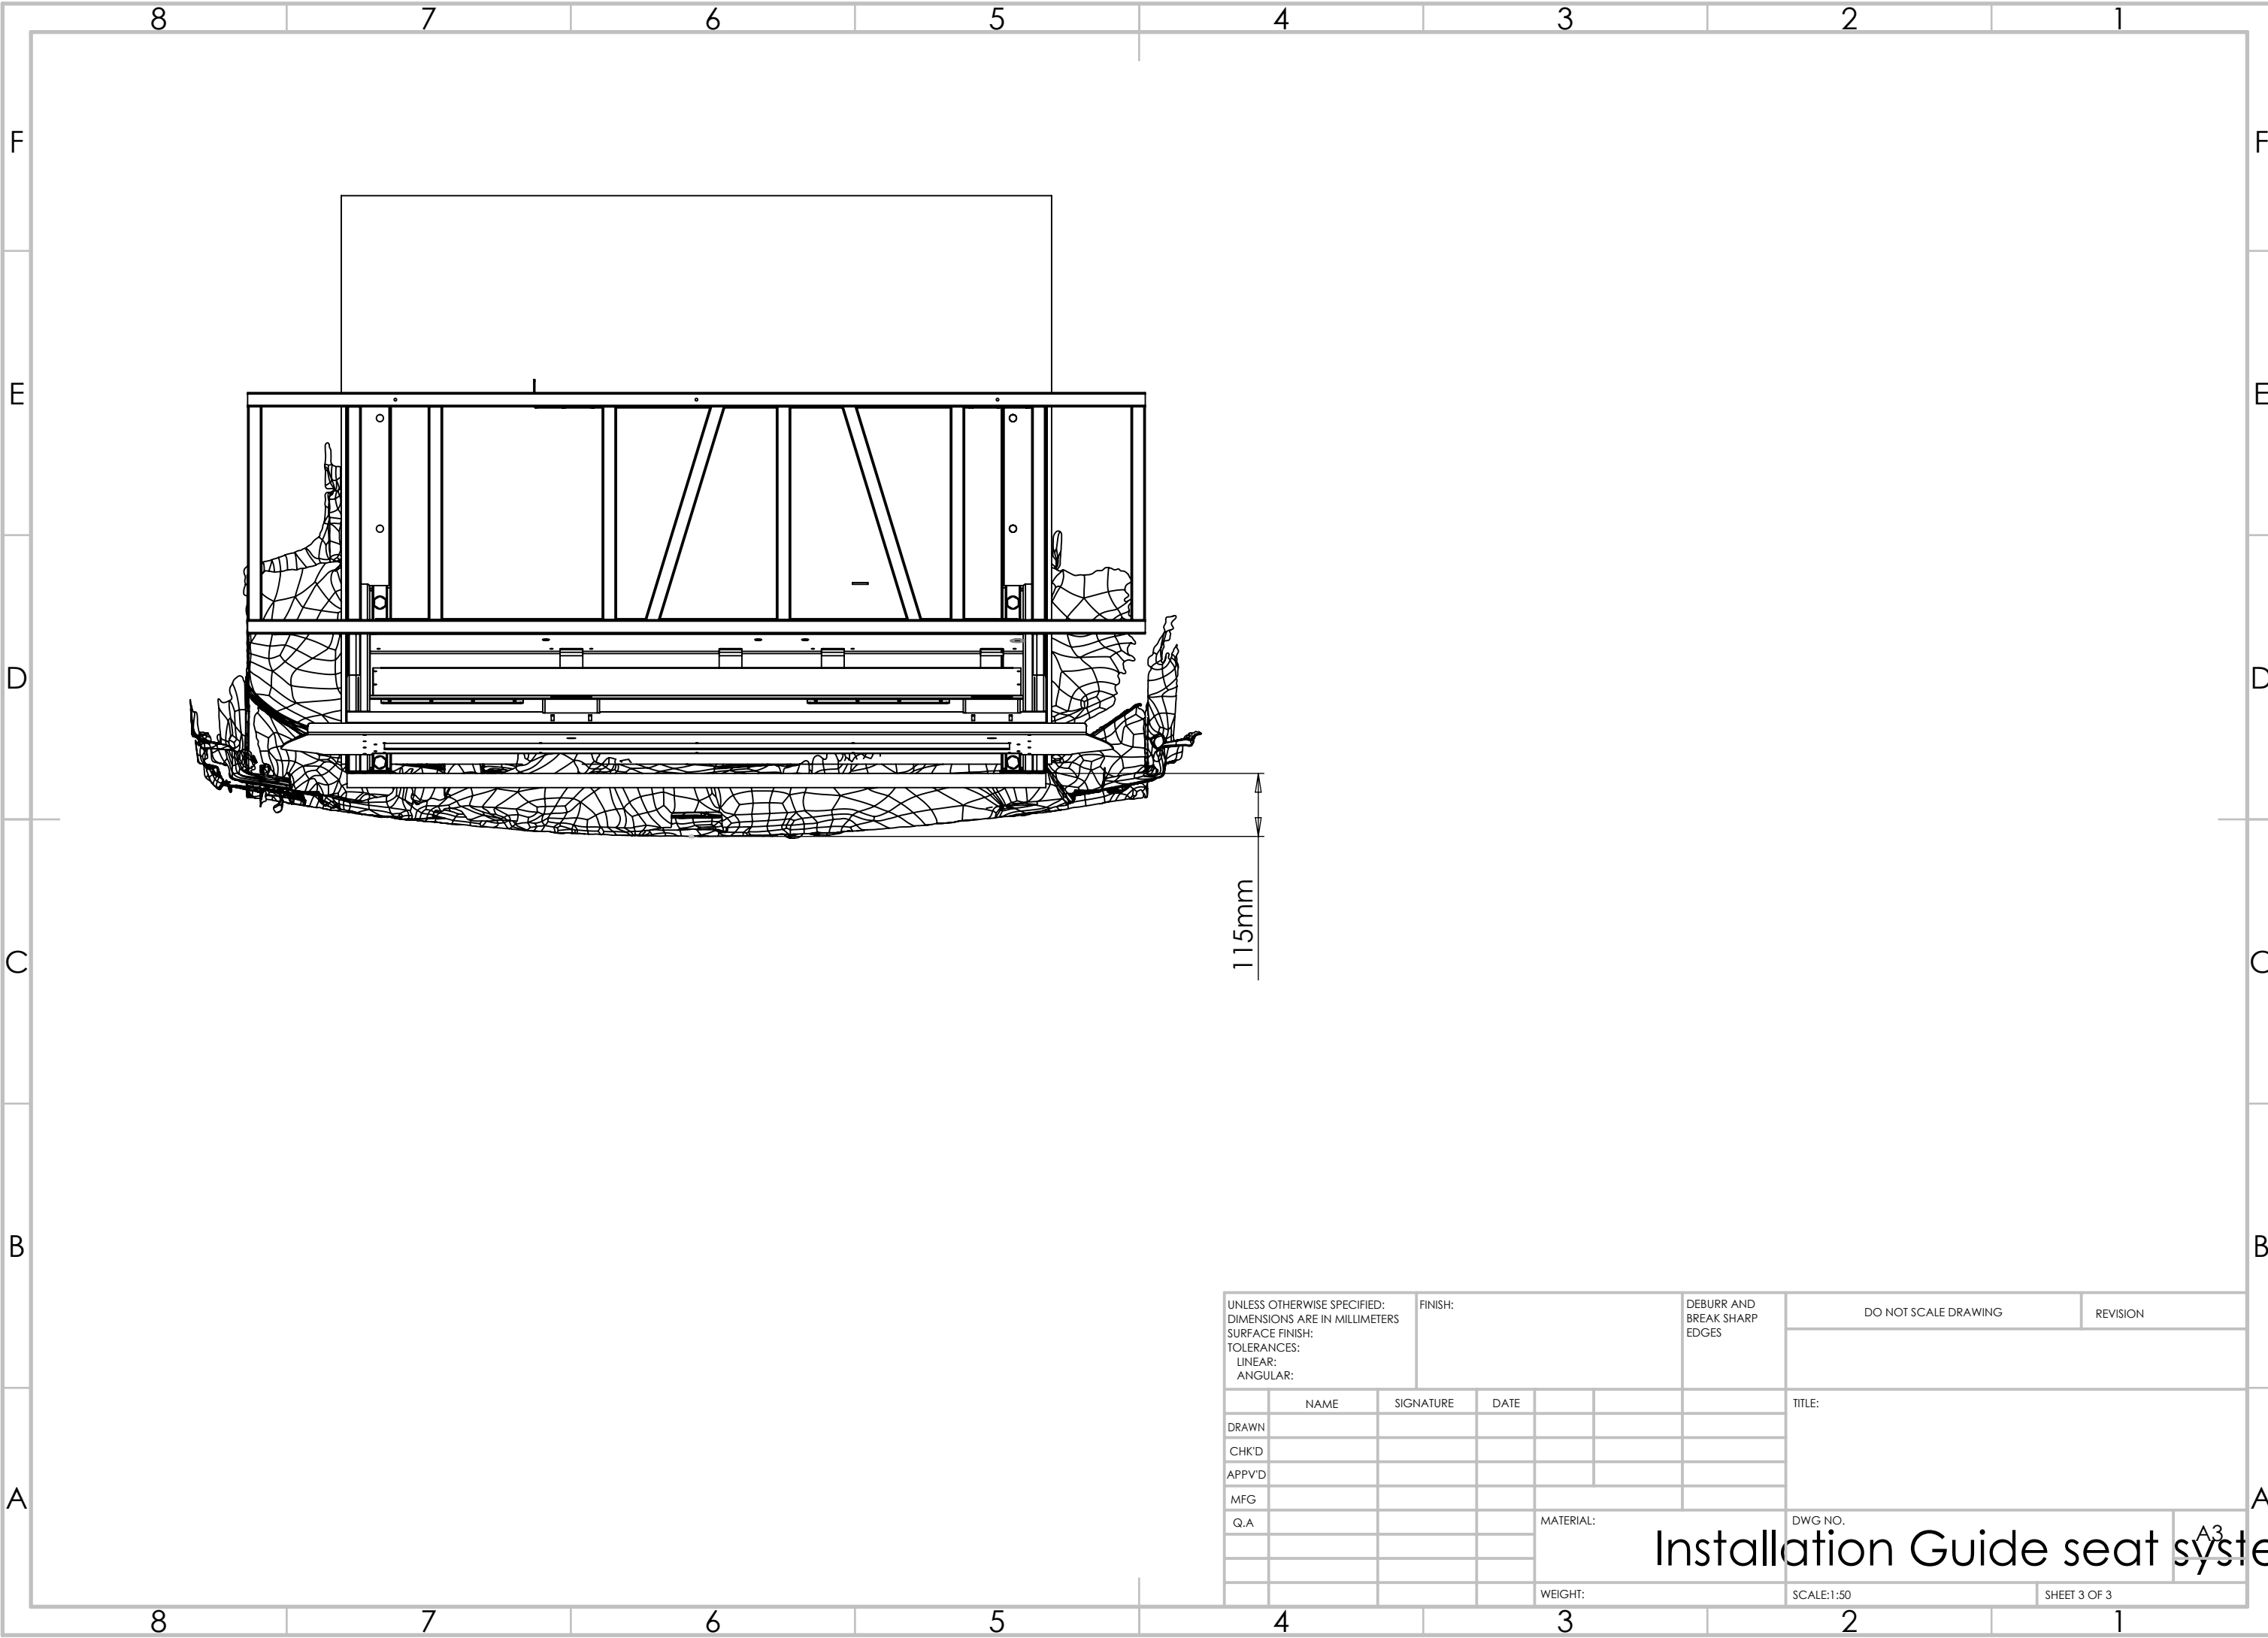

|   |      |           |      |         |  |                                    |           |                      |            |          |              |  |
|---|------|-----------|------|---------|--|------------------------------------|-----------|----------------------|------------|----------|--------------|--|
| UNLESS OTHERWISE SPECIFIED:<br>DIMENSIONS ARE IN MILLIMETERS<br>SURFACE FINISH:<br>TOLERANCES:<br>LINEAR:<br>ANGULAR: |      |           |      | FINISH: |  | DEBURR AND<br>BREAK SHARP<br>EDGES |           | DO NOT SCALE DRAWING |            | REVISION |              |  |
|   |      |           |      |         |  |                                    |           |                      |            |          |              |  |
|   | NAME | SIGNATURE | DATE |         |  |                                    | TITLE:    |                      |            |          |              |  |
| DRAWN   |      |           |      |         |  |                                    |           |                      |            |          |              |  |
| CHK'D   |      |           |      |         |  |                                    |           |                      |            |          |              |  |
| APPV'D   |      |           |      |         |  |                                    |           |                      |            |          |              |  |
| MFG   |      |           |      |         |  |                                    |           |                      |            |          |              |  |
| Q.A   |      |           |      |         |  |                                    | MATERIAL: |                      | DWG NO.    |          | A3           |  |
|   |      |           |      |         |  |                                    |           |                      |            |          |              |  |
|   |      |           |      |         |  |                                    | WEIGHT:   |                      | SCALE:1:50 |          | SHEET 3 OF 3 |  |

Installation Guide seat system